
EPLAN GmbH & Co. KG

An der alten Ziegelei 2
40789 Monheim am Rhein
Tel. +49 (0)2173 - 39 64 - 0

EPLAN Education

Bedrijf / klant	
Projectbeschrijving	Basisproject met coderingsstructuur volgens IEC-norm: Paginastructuur met functie aanduiding en locatie aand
Projectnummer	IEC_bas001
Opdrachtgever	EPLAN
Fabrikant (bedrijf)	EPLAN GmbH & Co. KG
Pad	EPLAN voorbeeldproject
Projectnaam	3-fase motor
Fabrikaat	
Type	
Installatieplaats	
Projectleider	
Deelbijzonderheid	


Gemaakt op	25-2-2026		
Bewerkt op	12-4-2026	Van (afkorting) Jarin	Aantal pagina's 10

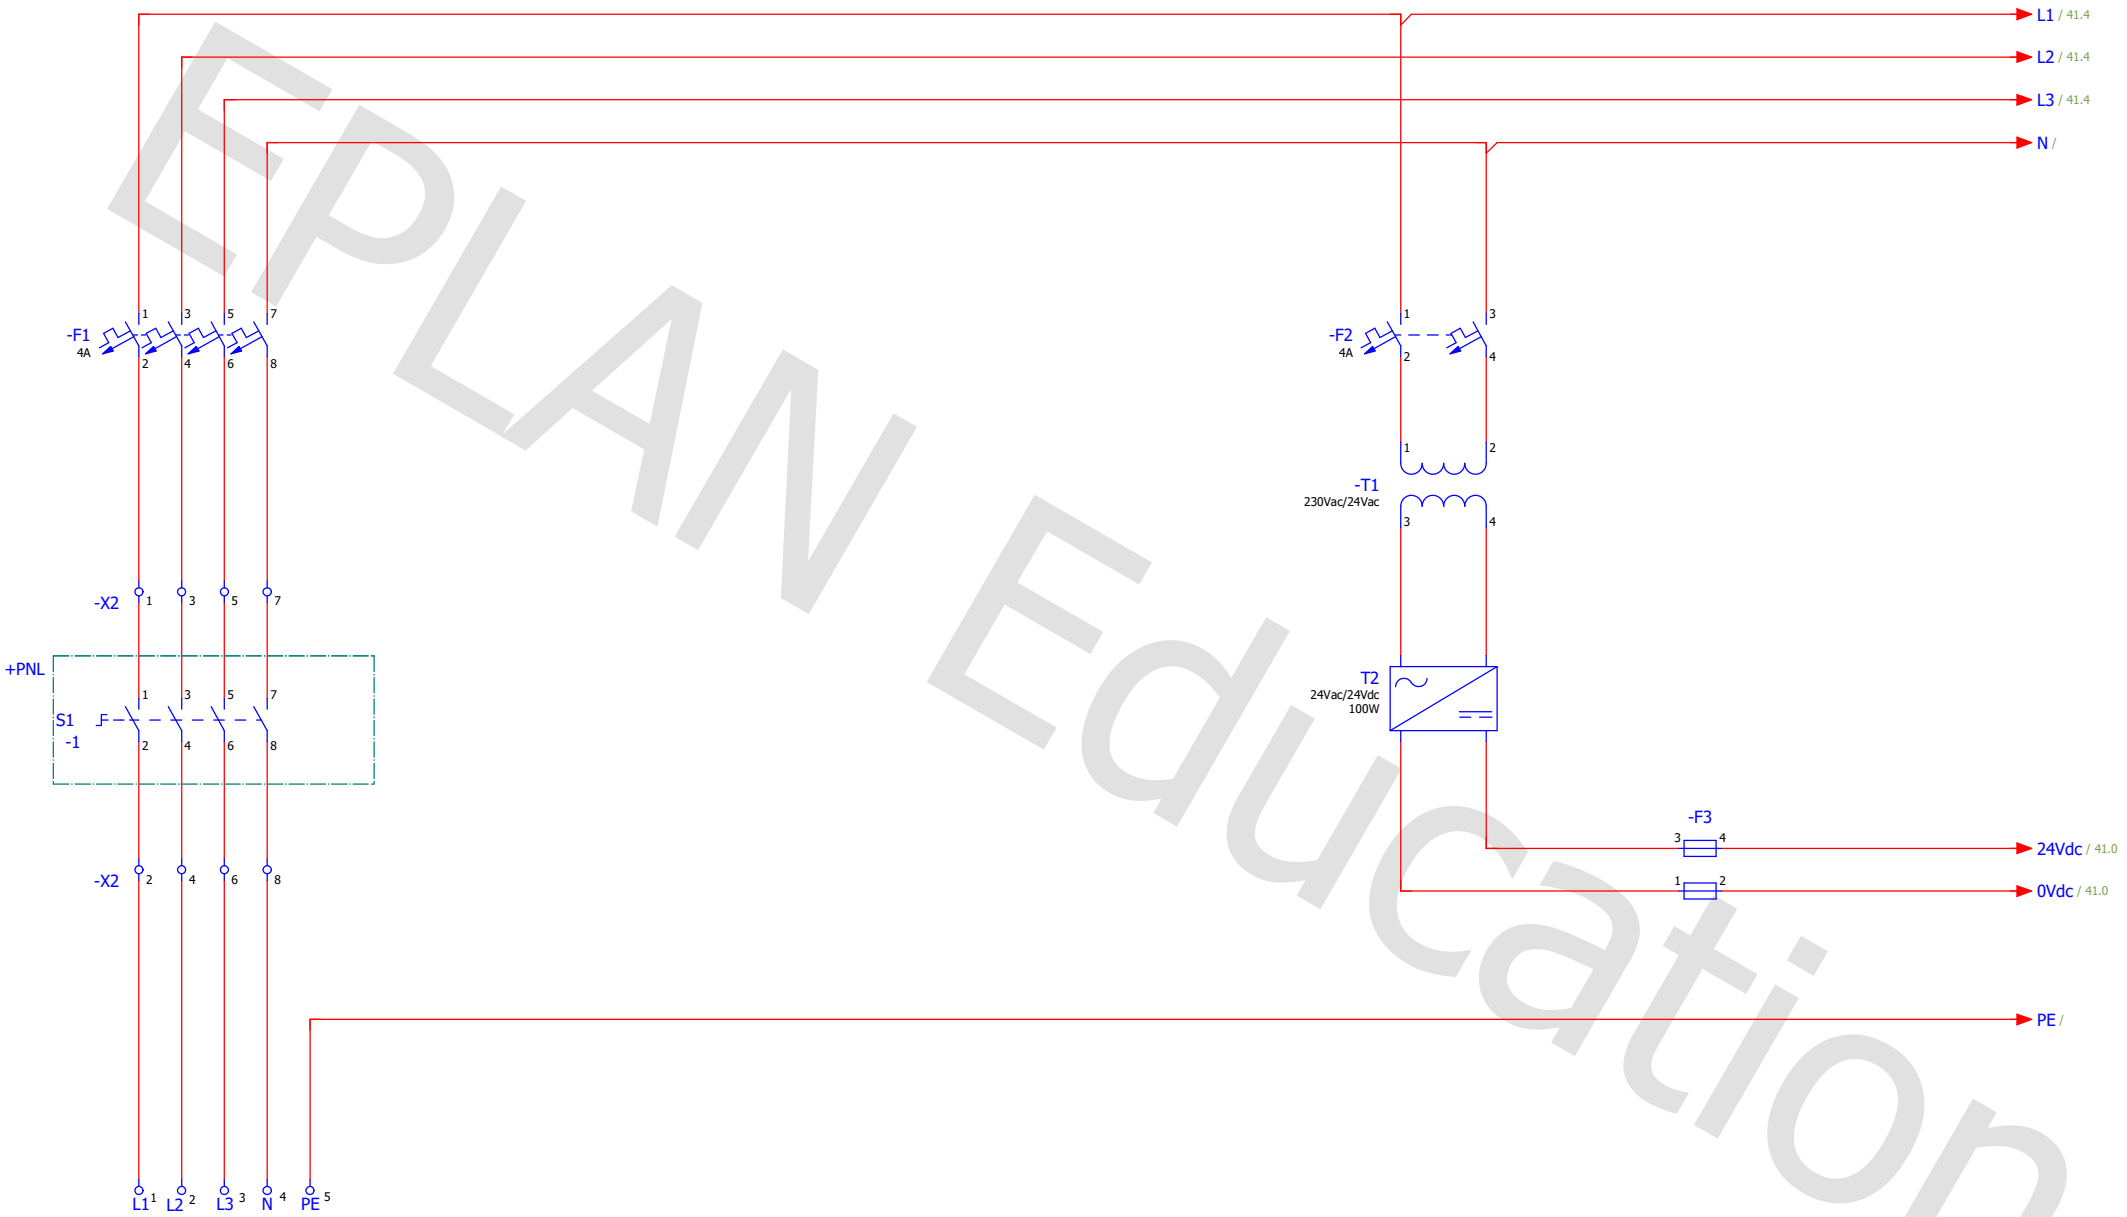

EPLAN Education


=CA1+EAA/1

			Datum	10-3-2026	EPLAN	EPLAN GmbH & Co. KG	voeding		= PWR
			Bew.	Jarin					+ ESK
			Gecontr.		Basisproject met coderingsstructuur volgens IEC-norm: Paginastructuur met functie aanduiding en locatie aanduiding			IEC_bas001	Blad 40
Wijziging	Datum	Naam	Oorspr.		Vervanging van	Vervangen door			Pagina 2 / 10

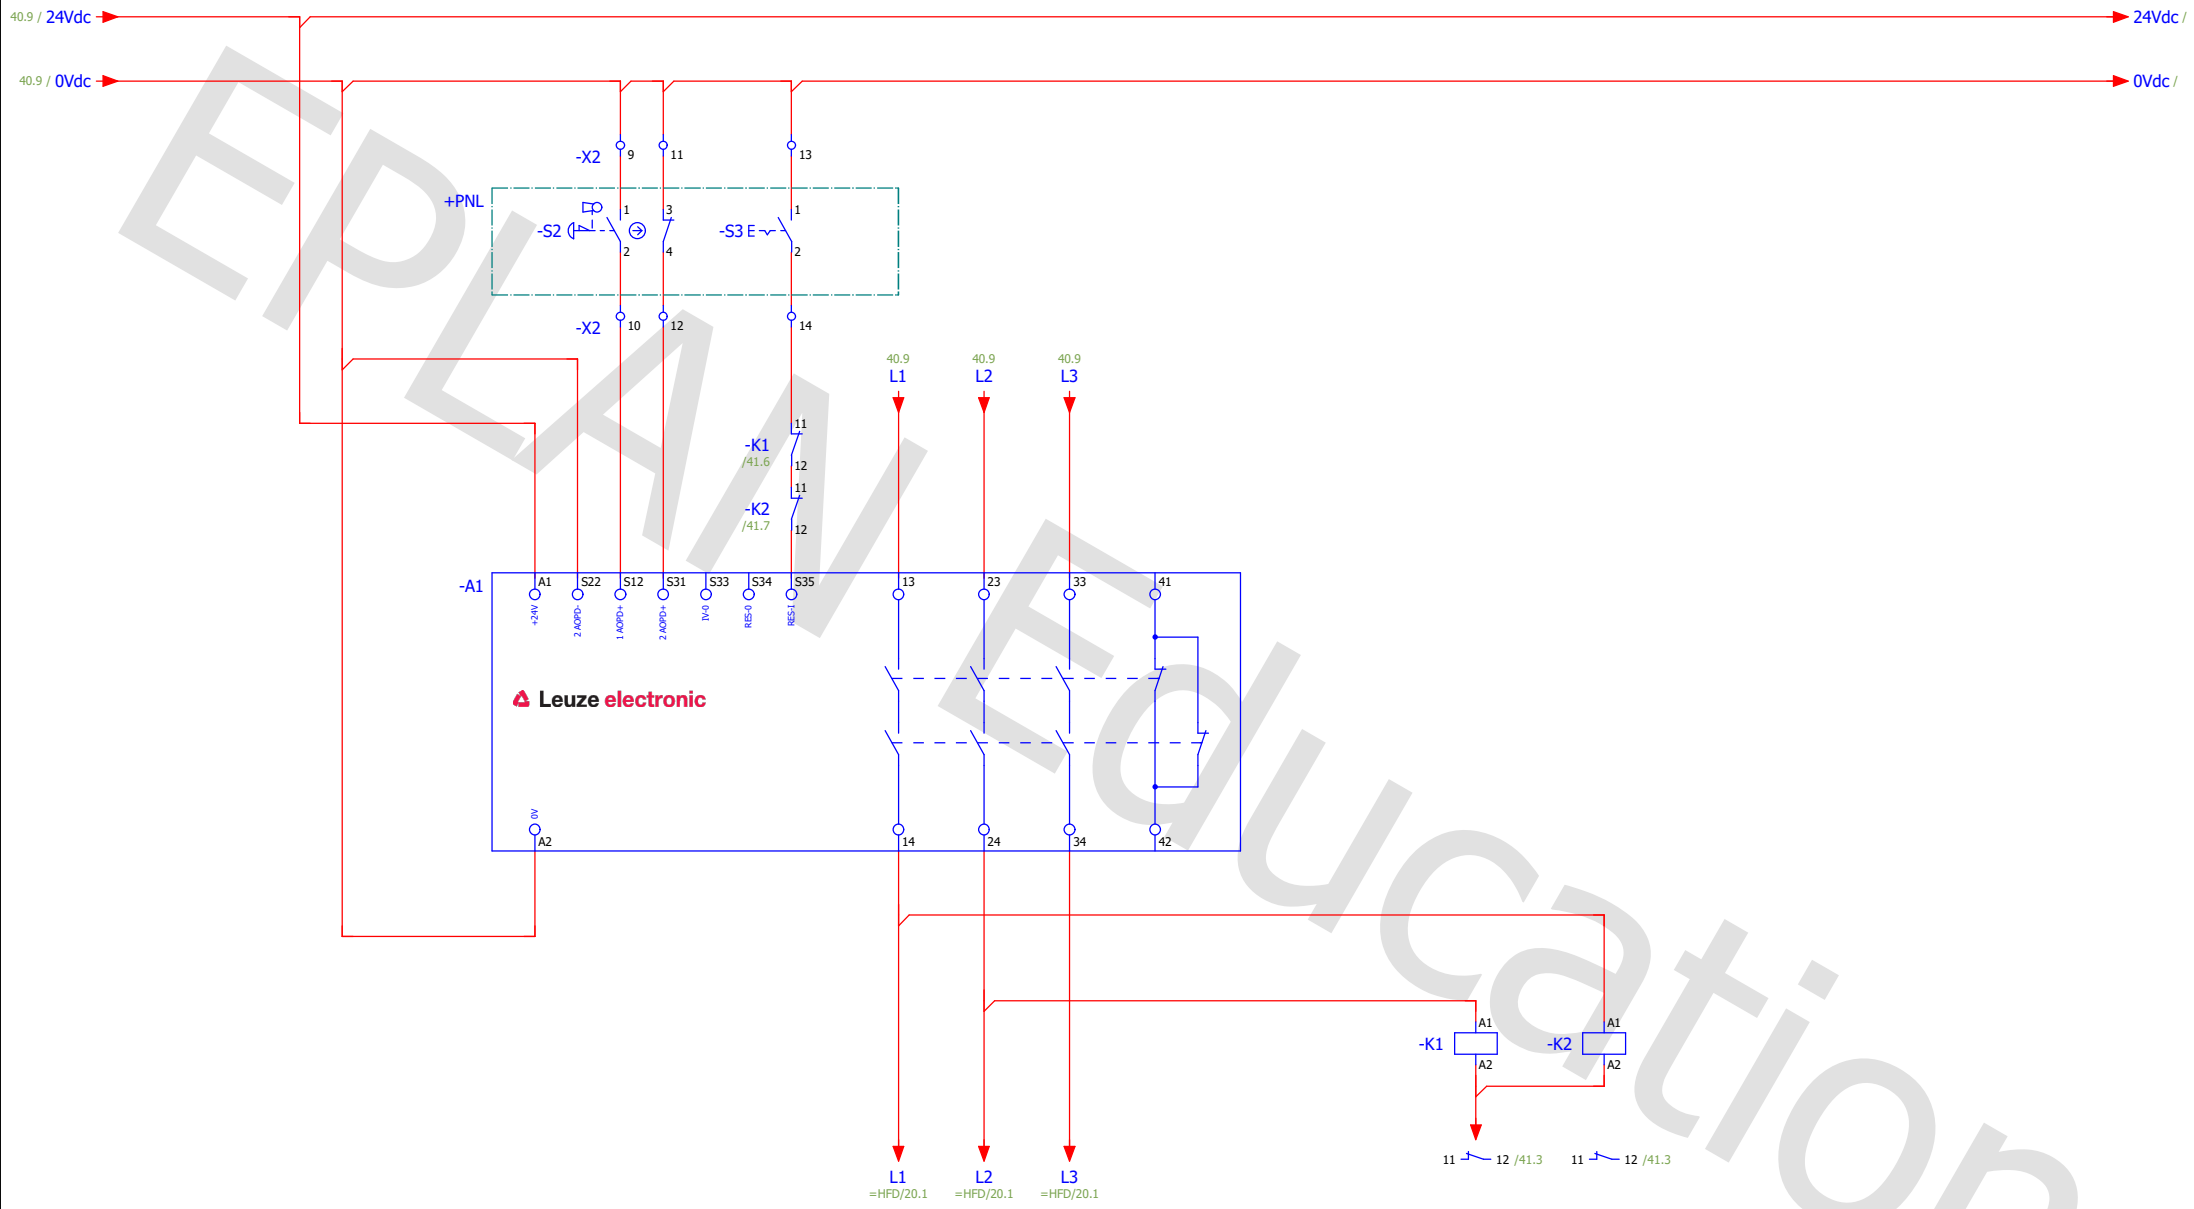

EPLAN Education


			Datum	17-3-2026	EPLAN	EPLAN GmbH & Co. KG	voeding	= PWR	
			Bew.	Jarin				+ ESK	
			Gecontr.		Basisproject met coderingsstructuur volgens IEC-norm: Paginastructuur met functie aanduiding en locatie aanduiding			IEC_bas001	Blad 41
Wijziging	Datum	Naam	Oorspr.		Vervanging van	Vervangen door			Pagina 3 / 10

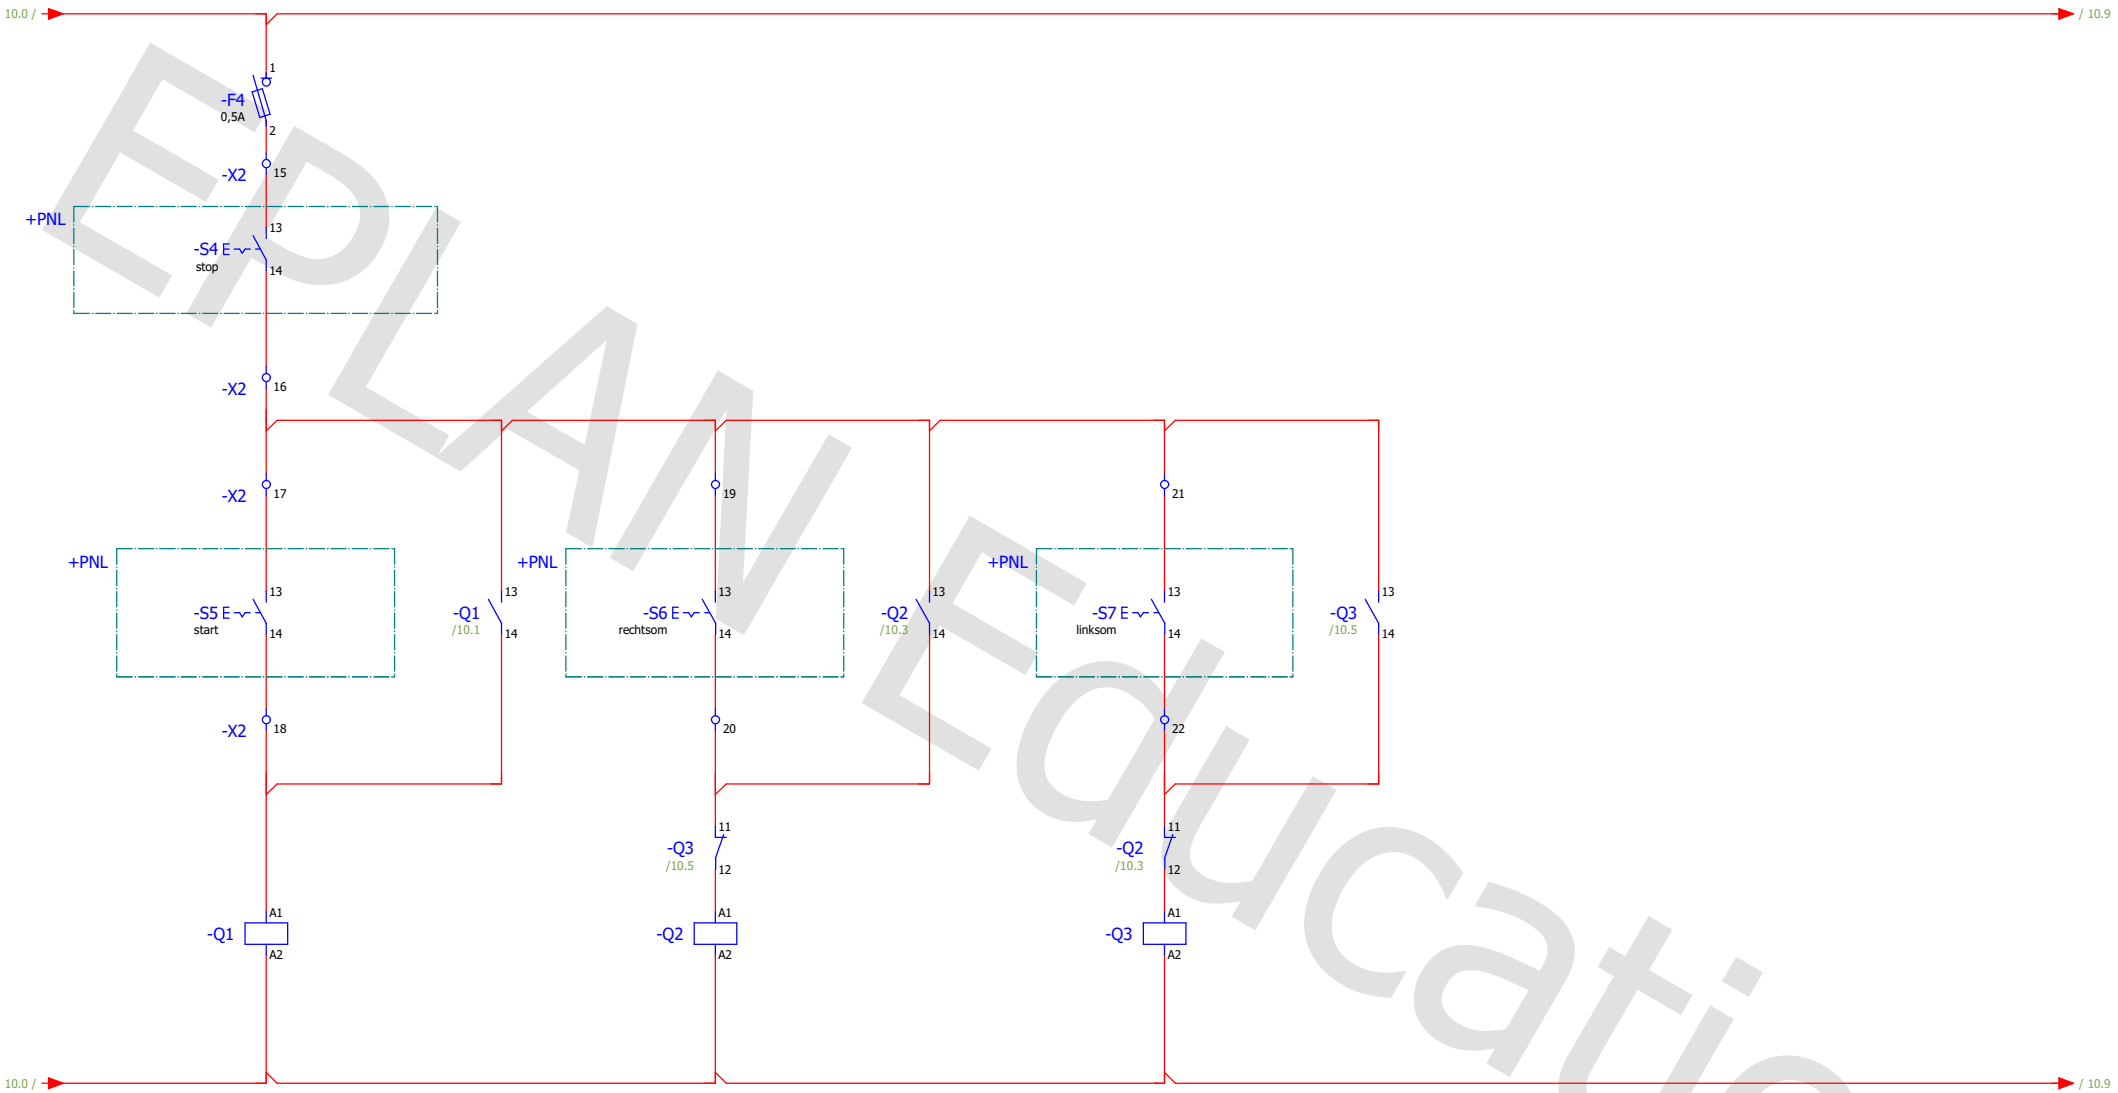

EPLAN Education


=PWR/41

			Datum	12-4-2026	EPLAN	EPLAN GmbH & Co. KG	Aan-uit omkeer sturing	= STR	
			Bew.	Jarin				+ ESK	
			Gecontr.		Basisproject met coderingsstructuur volgens IEC-norm: Paginastructuur met functie aanduiding en locatie aanduiding			IEC_bas001	Blad 10
Wijziging	Datum	Naam	Oorspr.		Vervanging van	Vervangen door			Pagina 4 / 10

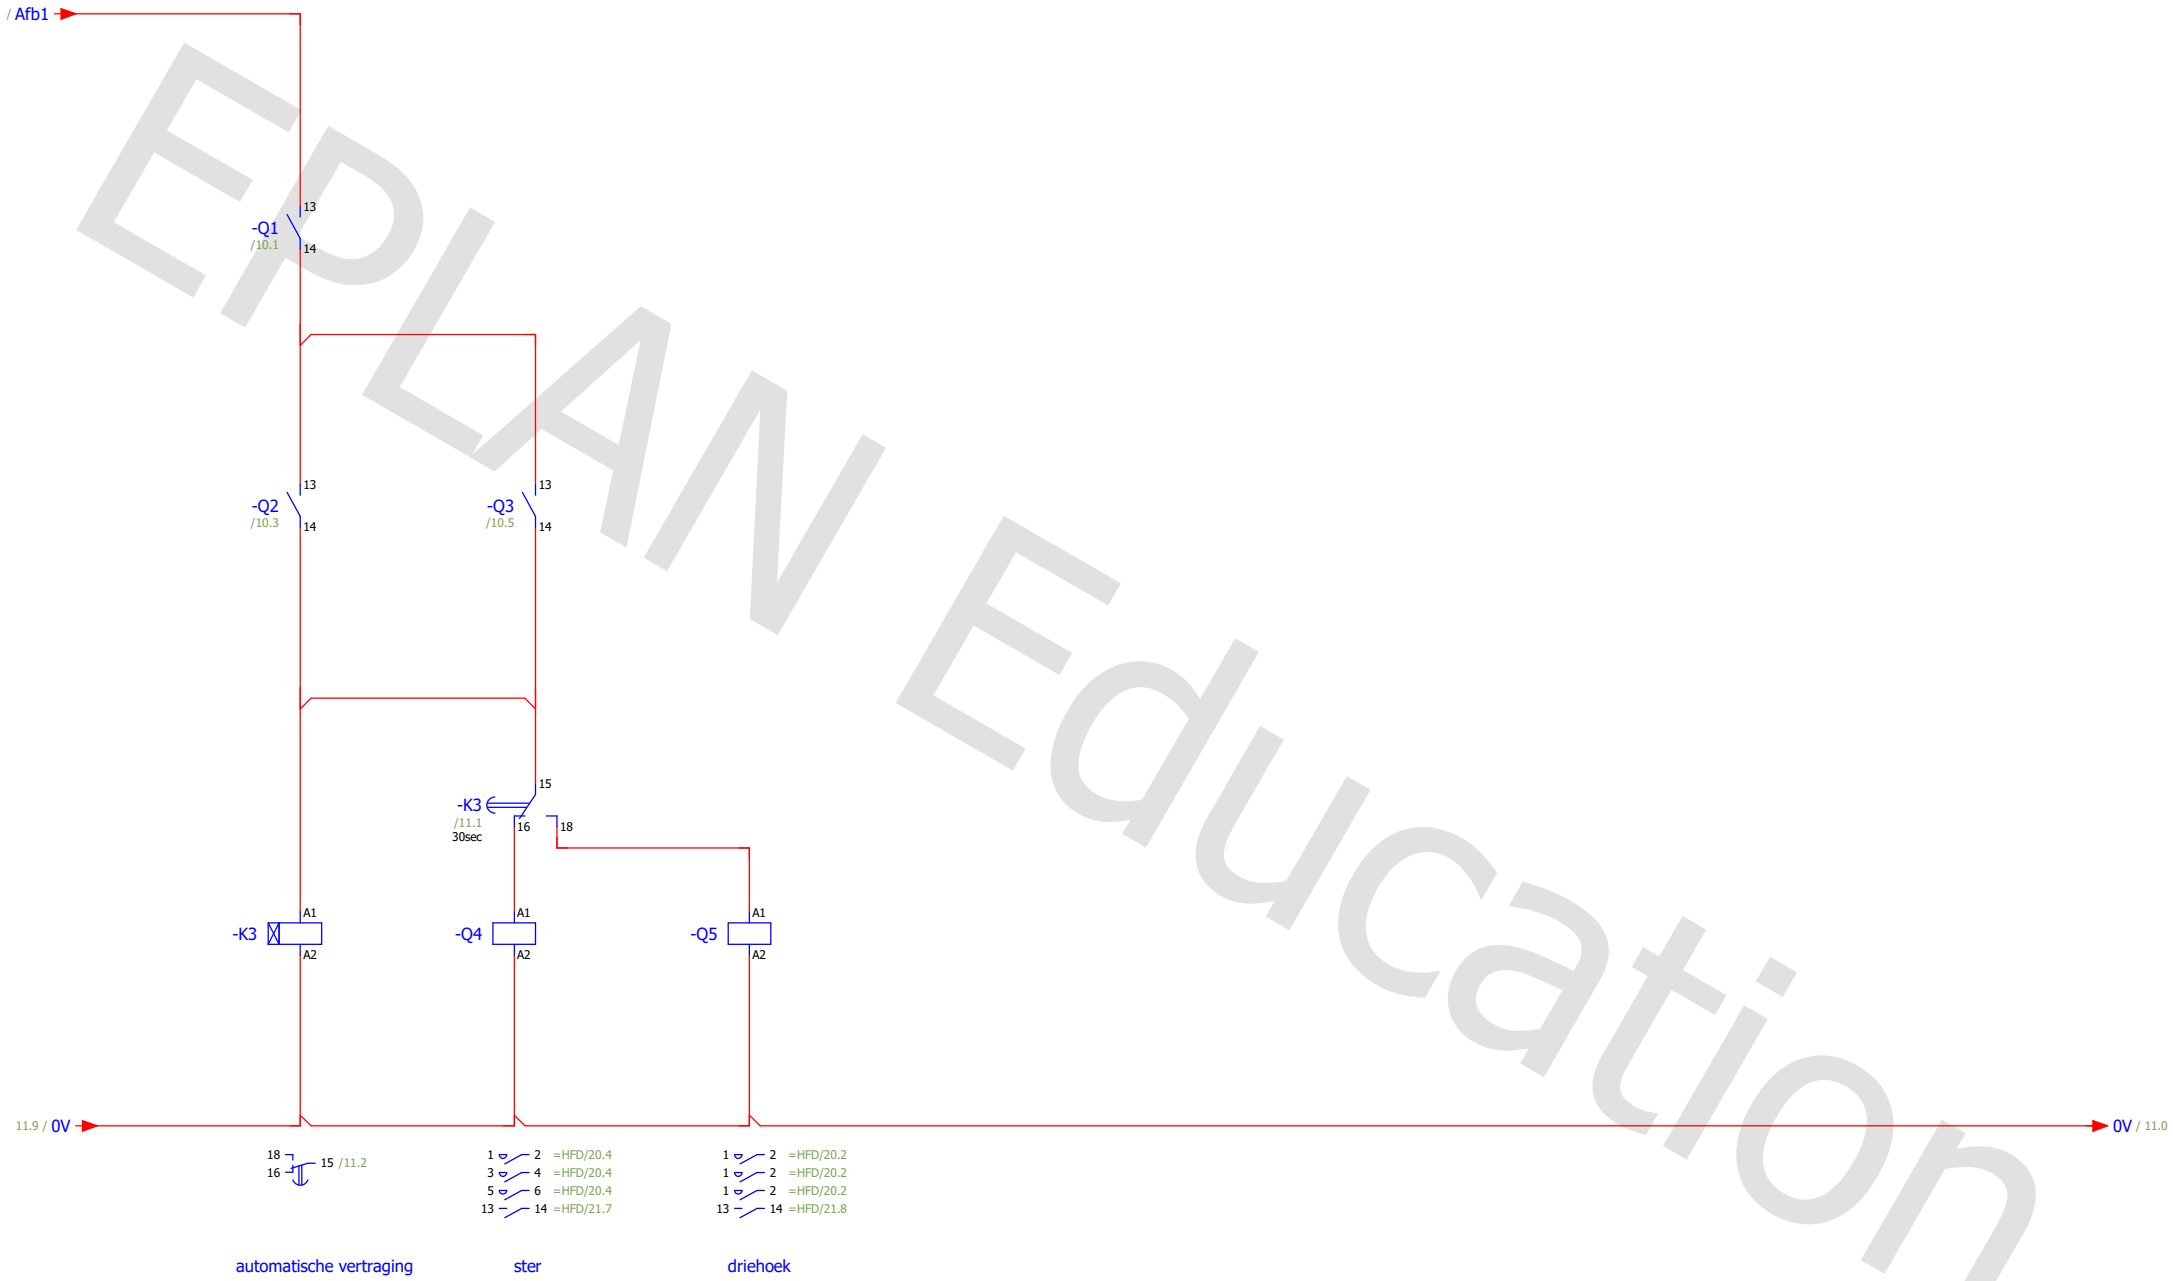

EPLAN Education

			Datum	12-4-2026	EPLAN	EPLAN GmbH & Co. KG	Aan-uit omkeer sturing	= STR	
			Bew.	Jarin				+ ESK	
			Gecontr.		Basisproject met coderingsstructuur volgens IEC-norm: Paginastructuur met functie aanduiding en locatie aanduiding			IEC_bas001	Blad 11
Wijziging	Datum	Naam	Oorspr.		Vervanging van	Vervangen door			Pagina 5 / 10

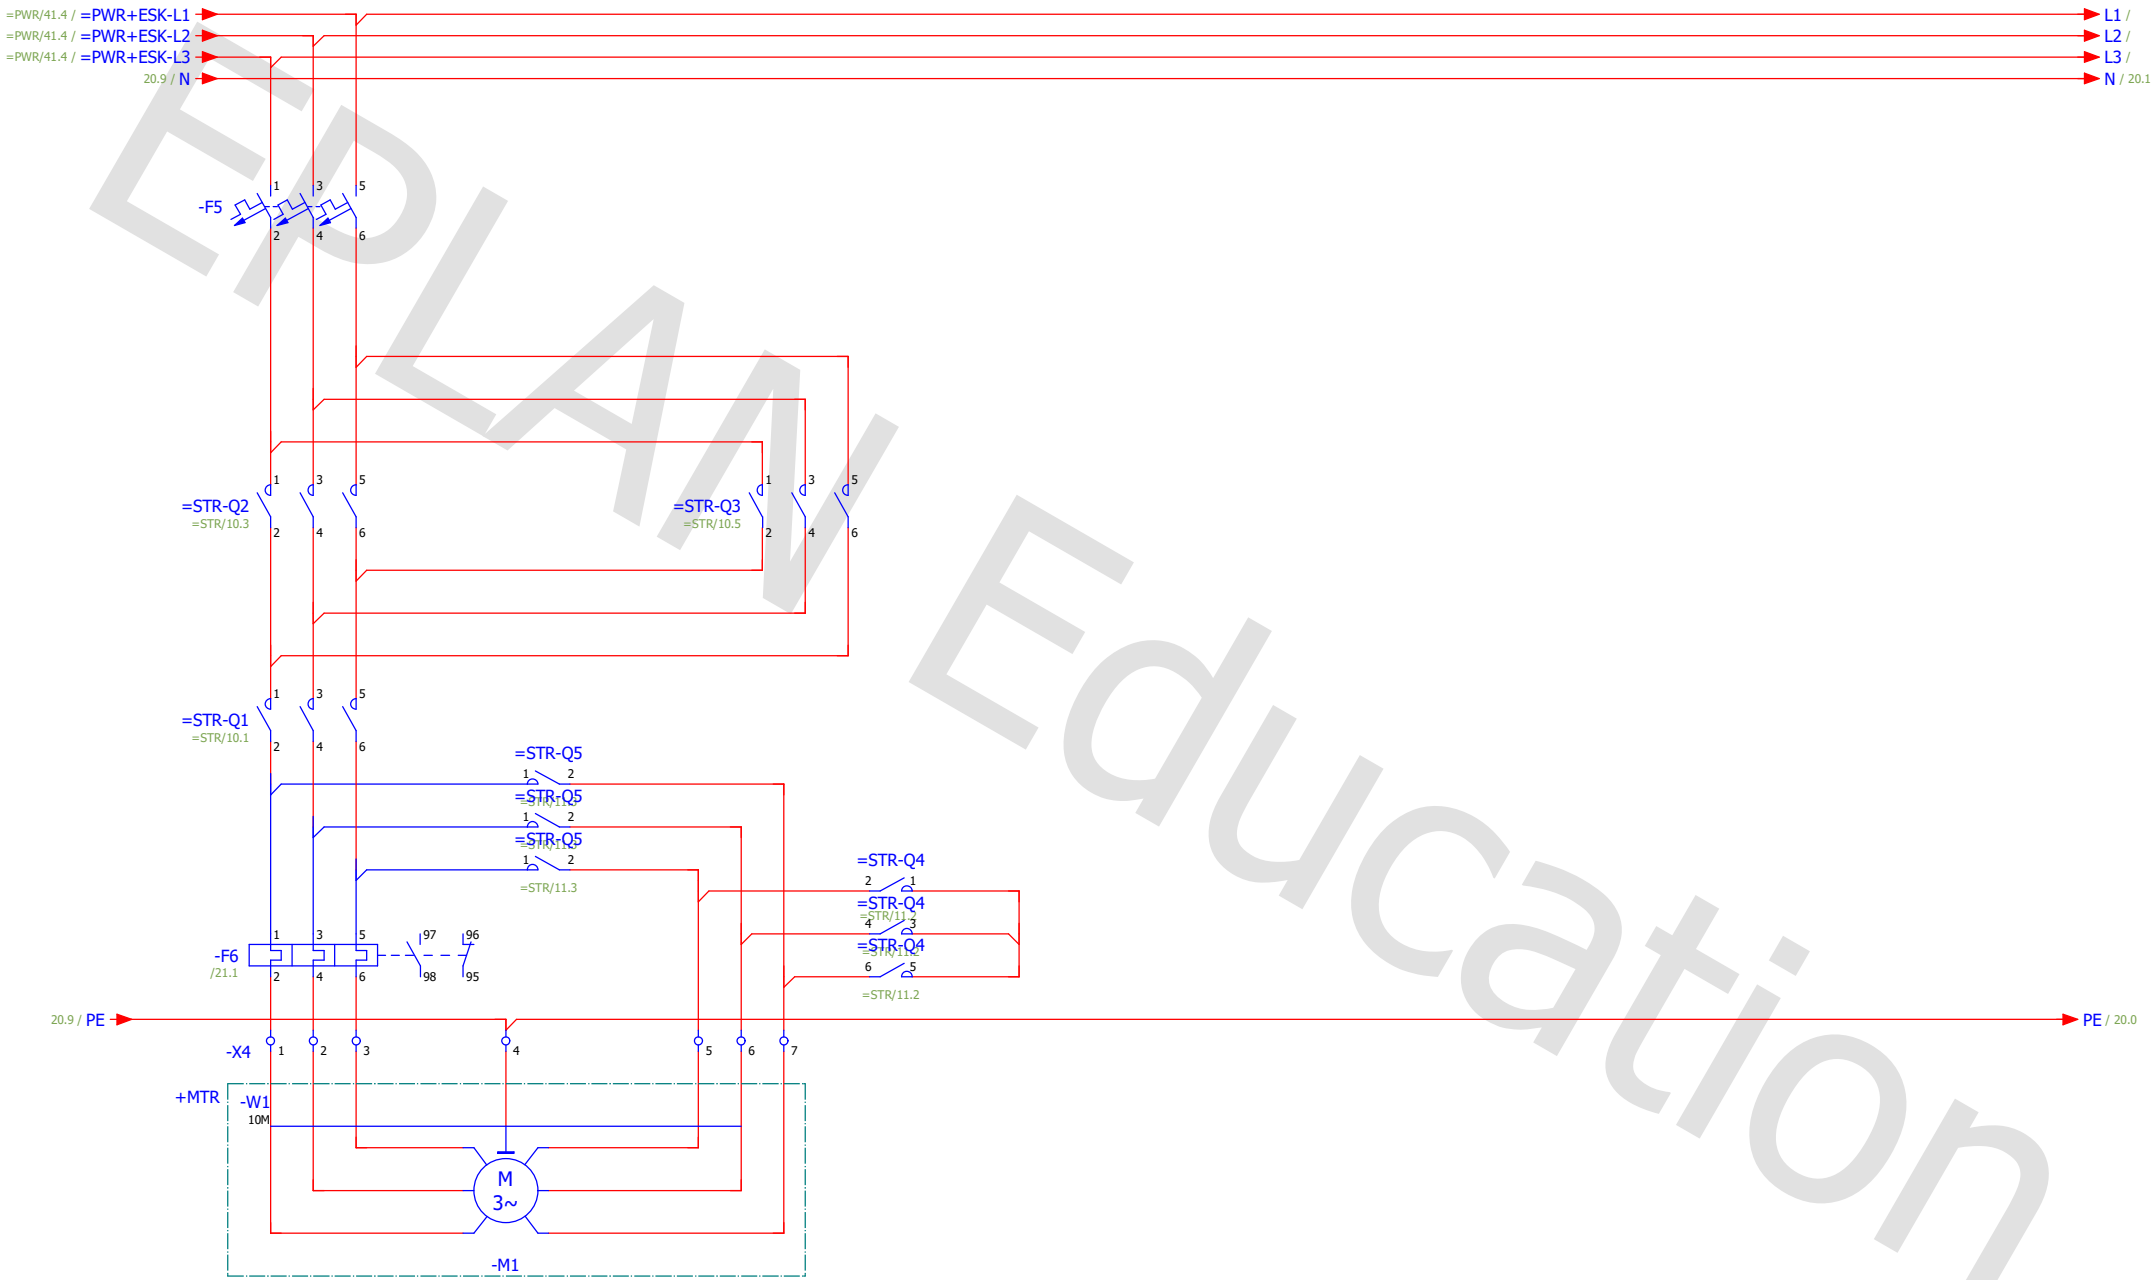


EPLAN Education

=STR/11

21

			Datum	12-4-2026	EPLAN	EPLAN GmbH & Co. KG	Aan - uit omkeer sturing		= HFD	
			Bew.	Jarin					+ ESK	
			Gecontr.		Basisproject met coderingsstructuur volgens IEC-norm: Paginastructuur met functie aanduiding en locatie aanduiding			IEC_bas001	Blad	20
Wijziging	Datum	Naam	Oorspr.		Vervanging van	Vervangen door			Pagina	6 / 10

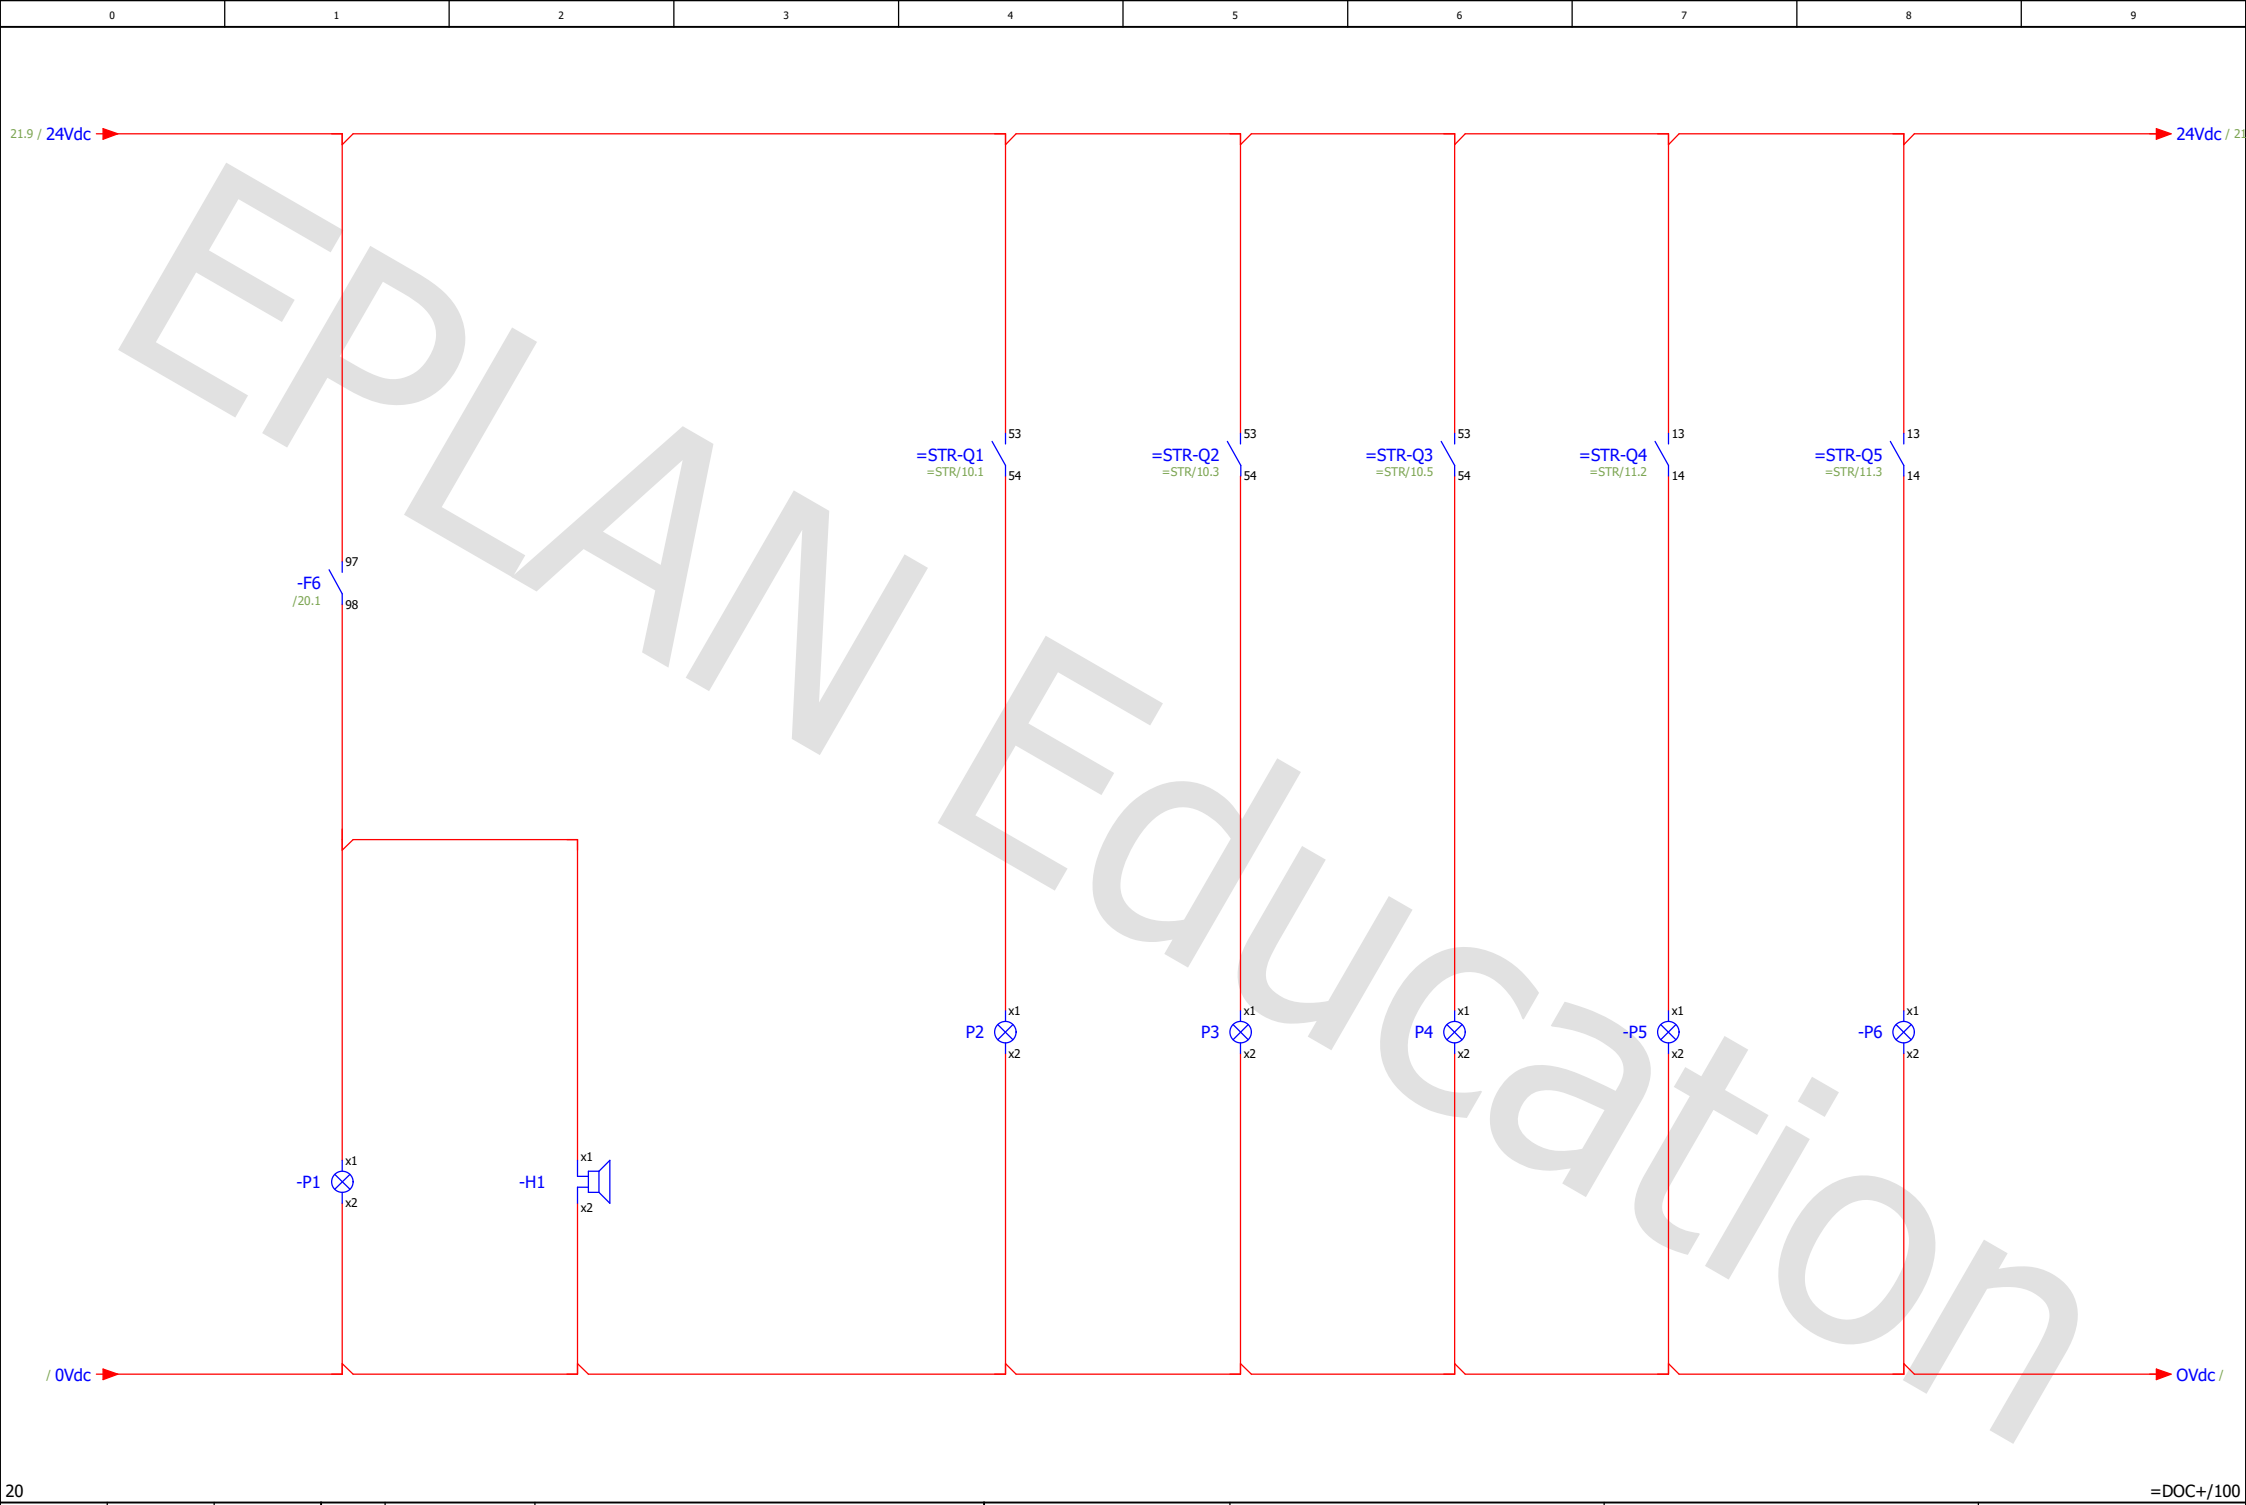

EPLAN Education

			Datum	12-4-2026	EPLAN	EPLAN GmbH & Co. KG	Aan - uit omkeer sturing	= HFD	
			Bew.	Jarin				+ ESK	
			Gecontr.		Basisproject met coderingsstructuur volgens IEC-norm: Paginastructuur met functie aanduiding en locatie aanduiding			IEC_bas001	Blad 21
Wijziging	Datum	Naam	Oorspr.		Vervanging van	Vervangen door			Pagina 7 / 10

Artikellijst

F01_001

Onderdeelcode	Hoeveelheid	Code	Typenummer	Leverancier	Artikelnummer
=PWR+ESK-F1	1		A9F74204	SE	SE.A9F74204
=PWR+ESK-F2	1		A9F74204	SE	SE.A9F74204
=PWR+ESK-F3	0				
=PWR+ESK-T1	0				
=PWR+ESK-T2	0				
=PWR+PNL-S1	0				
=STR+ESK-F4	0				
=STR+ESK-Q1	0				
=STR+ESK-Q2	0				
=STR+ESK-Q3	0				
=STR+PNL-S4	0				
=STR+PNL-S5	0				
=STR+PNL-S6	0				
=STR+PNL-S7	0				
=HFD+ESK-F5	0				
=HFD+ESK-P2	0				
=HFD+ESK-P3	0				
=HFD+ESK-P5	0				
=HFD+MTR-M1	0				

EPLAN Education

Klemmenaansluitschema


F11_002
Jarin 10-3-2026

EPLAN Education

Interne doelen

=PWR+ESK-L1	
Bruggen	
Klem	
Aansluiting	1

Externe doelen

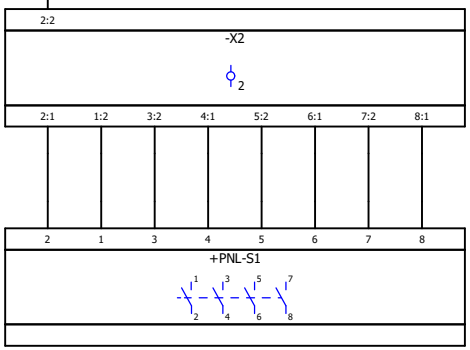

			Datum	10-3-2026	EPLAN	EPLAN GmbH & Co. KG	Klemmenaansluitschema =PWR+ESK-L1	= DOC	
			Bew.	Jarin				+	
			Gecontr.		Basisproject met coderingsstructuur volgens IEC-norm: Paginastructuur met functie aanduiding en locatie aanduiding			IEC_bas001	Blad 101
Wijziging	Datum	Naam	Oorspr.		Vervanging van	Vervangen door			Pagina 9 / 10

Kabeloverzicht

F10_001

Kabelnaam	Bron (van)	Doel (tot)	Kabeltype	alle aders	Gebruikte aders	Dwarsdoorsnede [mm]	Lengte [m]	Functietekst	Grafische pagina van de kabelaansluitlijst
=HFD+MTR-W1					0			10M	

EPLAN Education

			Datum	10-3-2026	EPLAN	EPLAN GmbH & Co. KG	Kabeloverzicht : =HFD+MTR-W1 - =HFD+MTR-W1		= DOC
			Bew.	Jarin					+
			Gecontr.		Basisproject met coderingsstructuur volgens IEC-norm: Paginastructuur met functie aanduiding en locatie aanduiding			IEC_bas001	Blad 102
Wijziging	Datum	Naam	Oorspr.		Vervanging van	Vervangen door			Pagina 10 / 10