EPLAN GmbH & Co. KG


An der alten Ziegelei 2
40789 Monheim am Rhein
Tel. +49 (0)2173 - 39 64 - 0

Bedrijf / klant	
Projectbeschrijving	Basisproject met coderingsstructuur volgens IEC-norm: Paginastructuur met functie aanduiding en locatie aand
Projectnummer	IEC_bas001
Opdrachtgever	EPLAN

Fabrikant (bedrijf)	EPLAN GmbH & Co. KG
Pad	EPLAN voorbeeldproject
Projectnaam	3-fase motor
Fabrikaat	
Type	
Installatieplaats	
Projectleider	
Deelbijzonderheid	

Gemaakt op	25-2-2026		
Bewerkt op	25-3-2026	Van (afkorting) htjid	Aantal pagina's 6


EPLAN Education

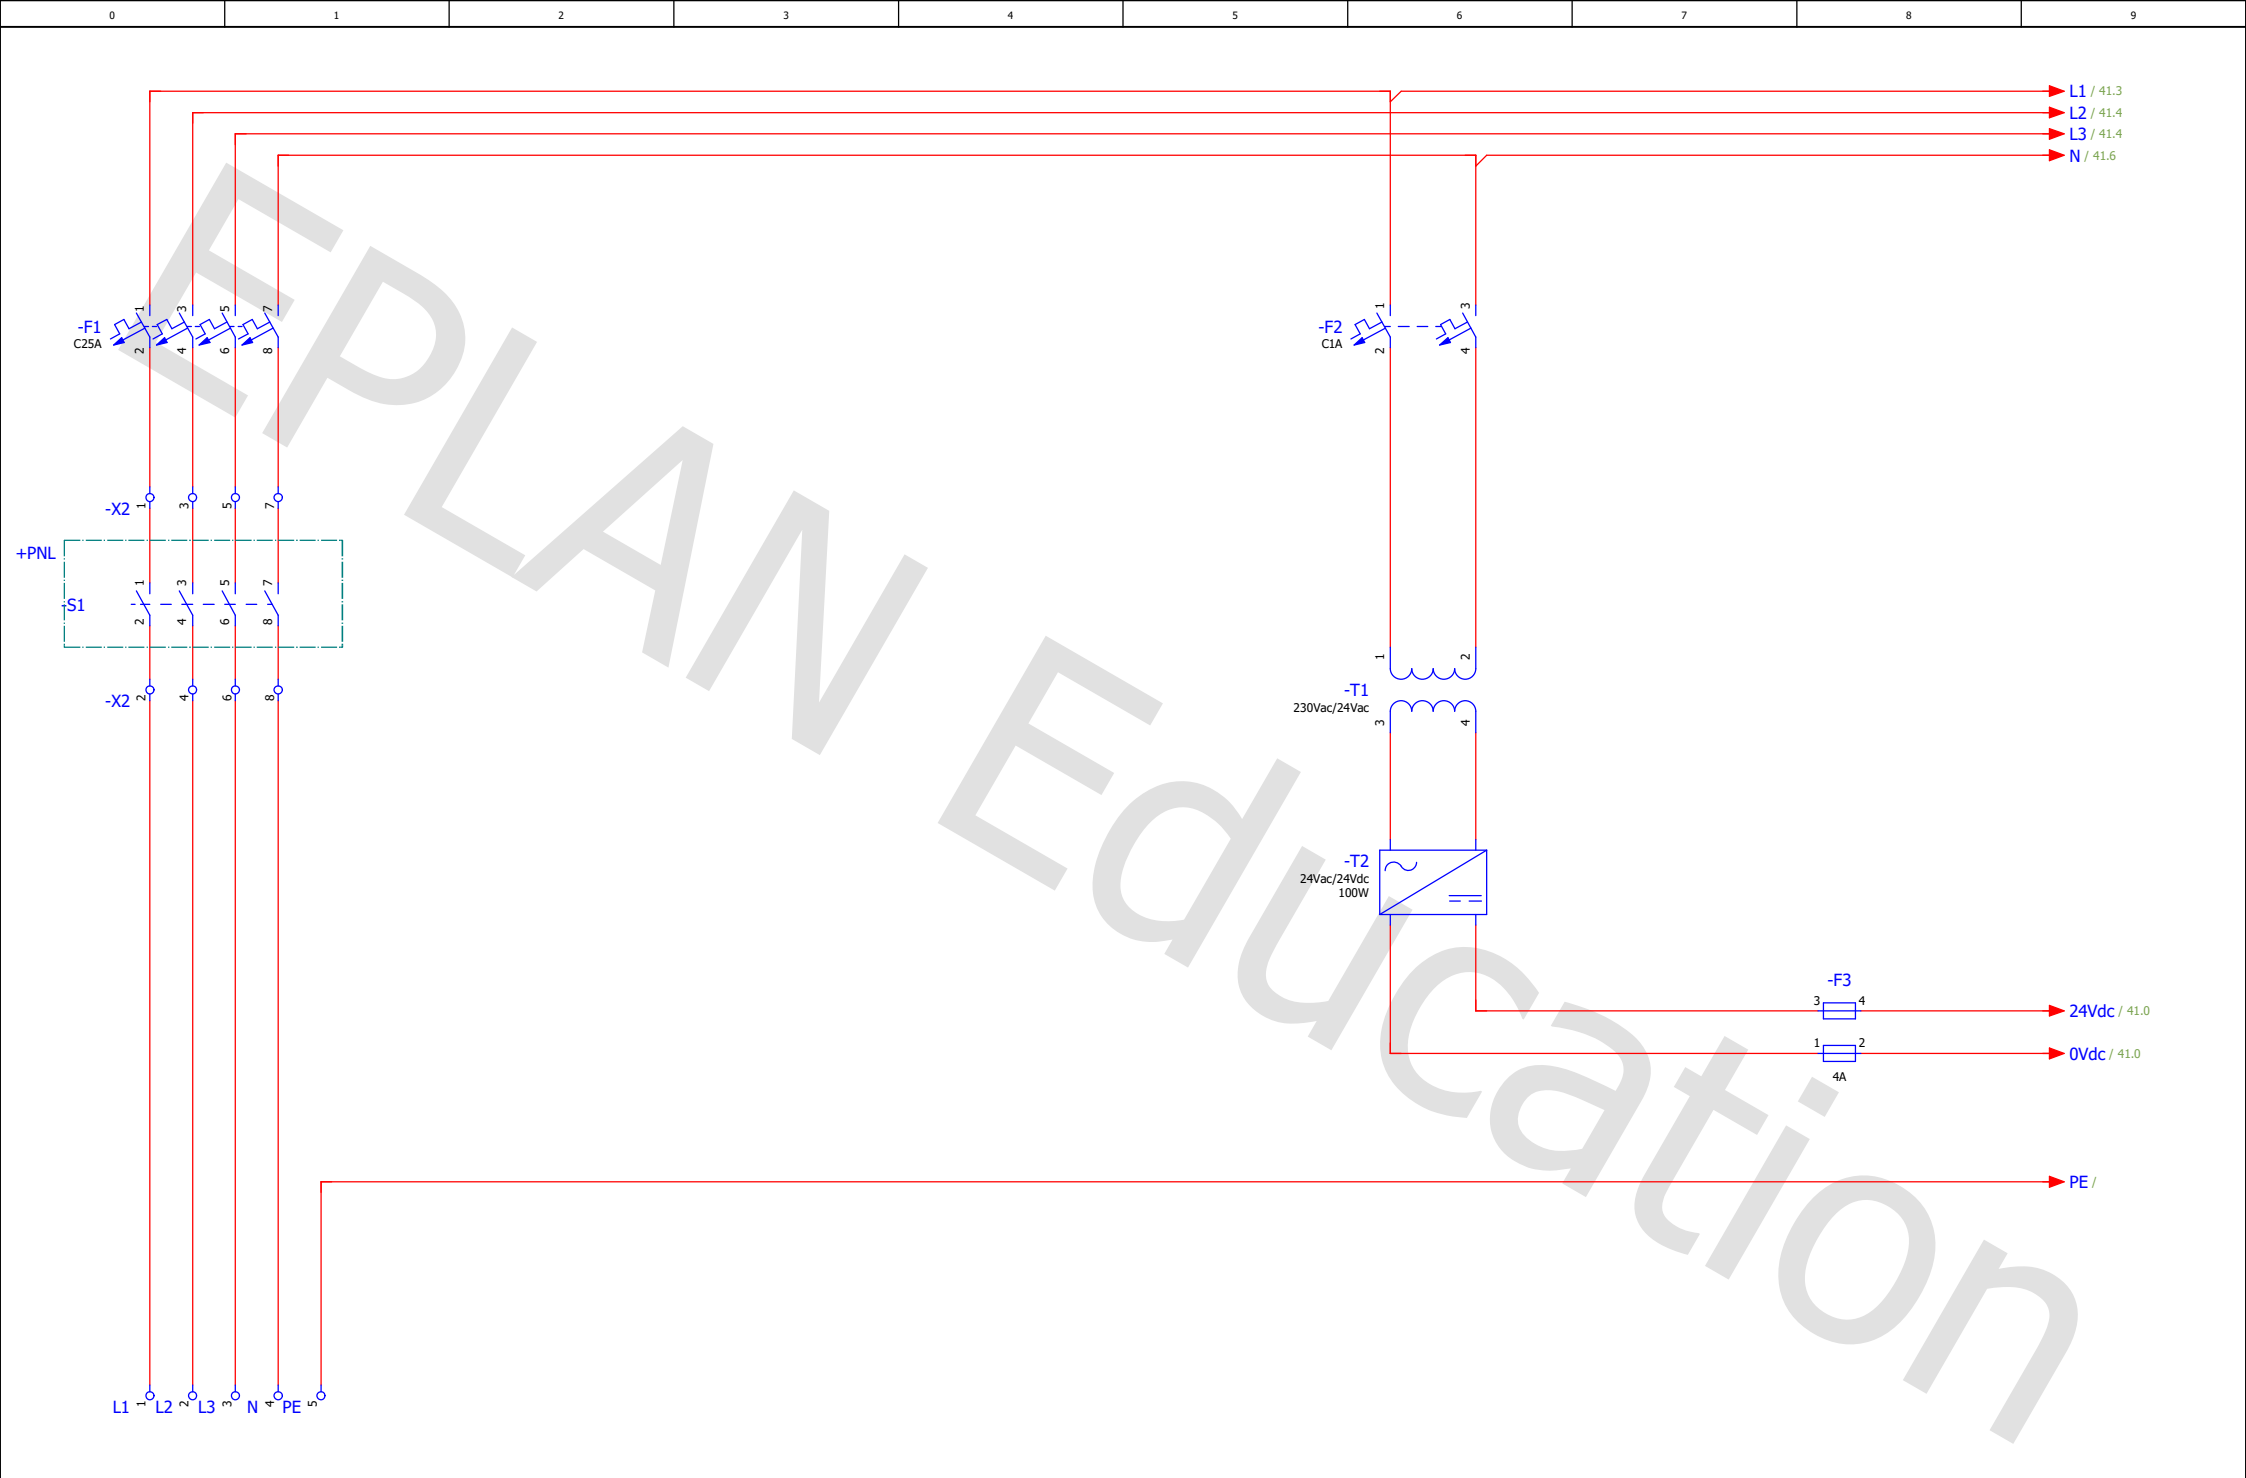

=CA1+EAA/1


41

			Datum	25-3-2026	EPLAN	EPLAN GmbH & Co. KG	Voeding		= PWR
			Bew.	htjid					+ ESK
			Gecontr.		Basisproject met coderingsstructuur volgens IEC-norm: Paginastructuur met functie aanduiding en locatie aanduiding			IEC_bas001	Blad 40
Wijziging	Datum	Naam	Oorspr.		Vervanging van	Vervangen door			Pagina 2 / 6

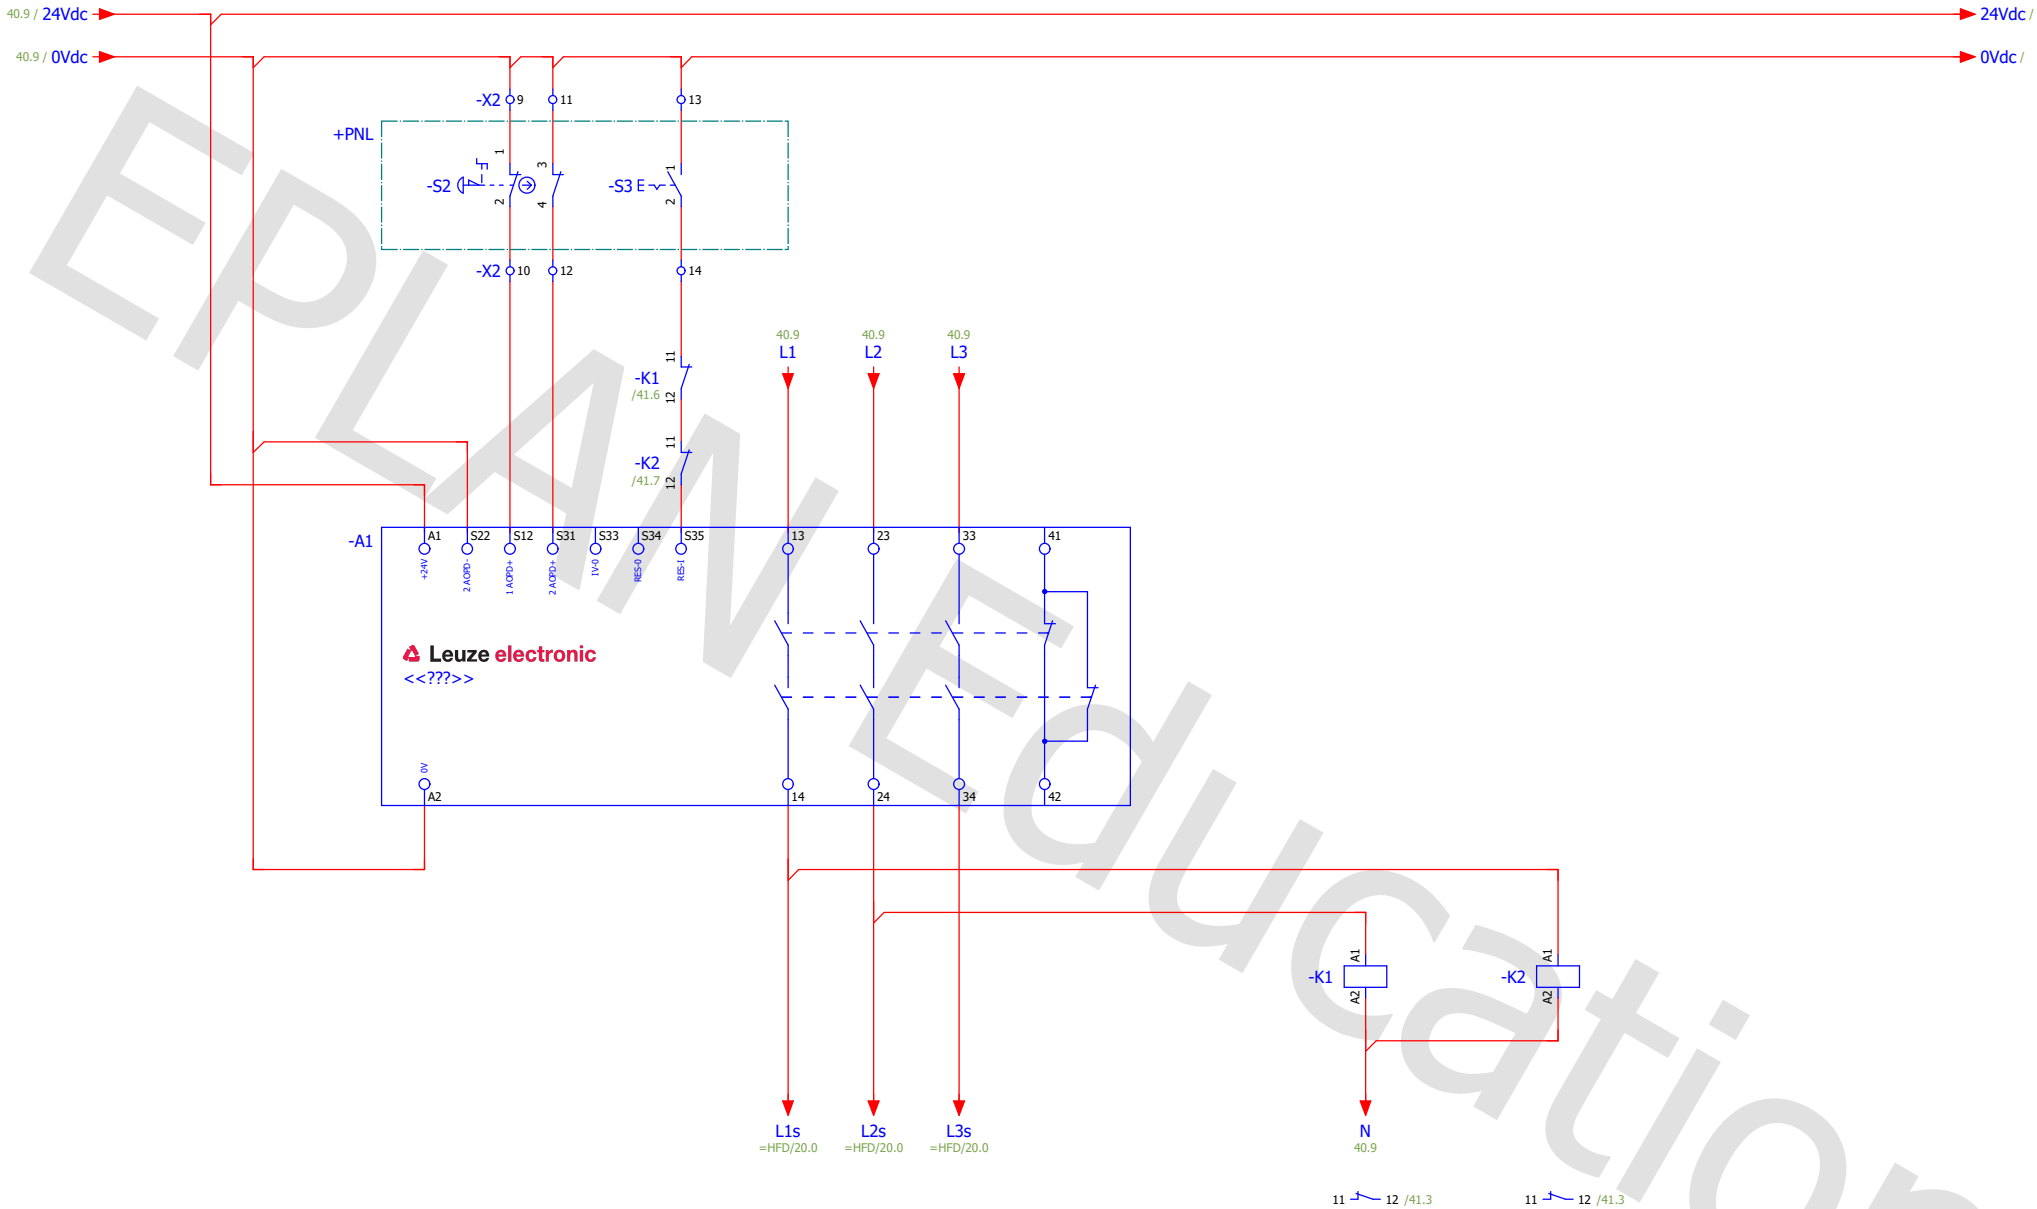

EPLAN Education


			Datum	25-3-2026	EPLAN	EPLAN GmbH & Co. KG	Noodstop		= PWR
			Bew.	htjid					+ ESK
			Gecontr.		Basisproject met coderingsstructuur volgens IEC-norm: Paginastructuur met functie aanduiding en locatie aanduiding			IEC_bas001	Blad 41
Wijziging	Datum	Naam	Oorspr.		Vervanging van	Vervangen door			Pagina 3 / 6

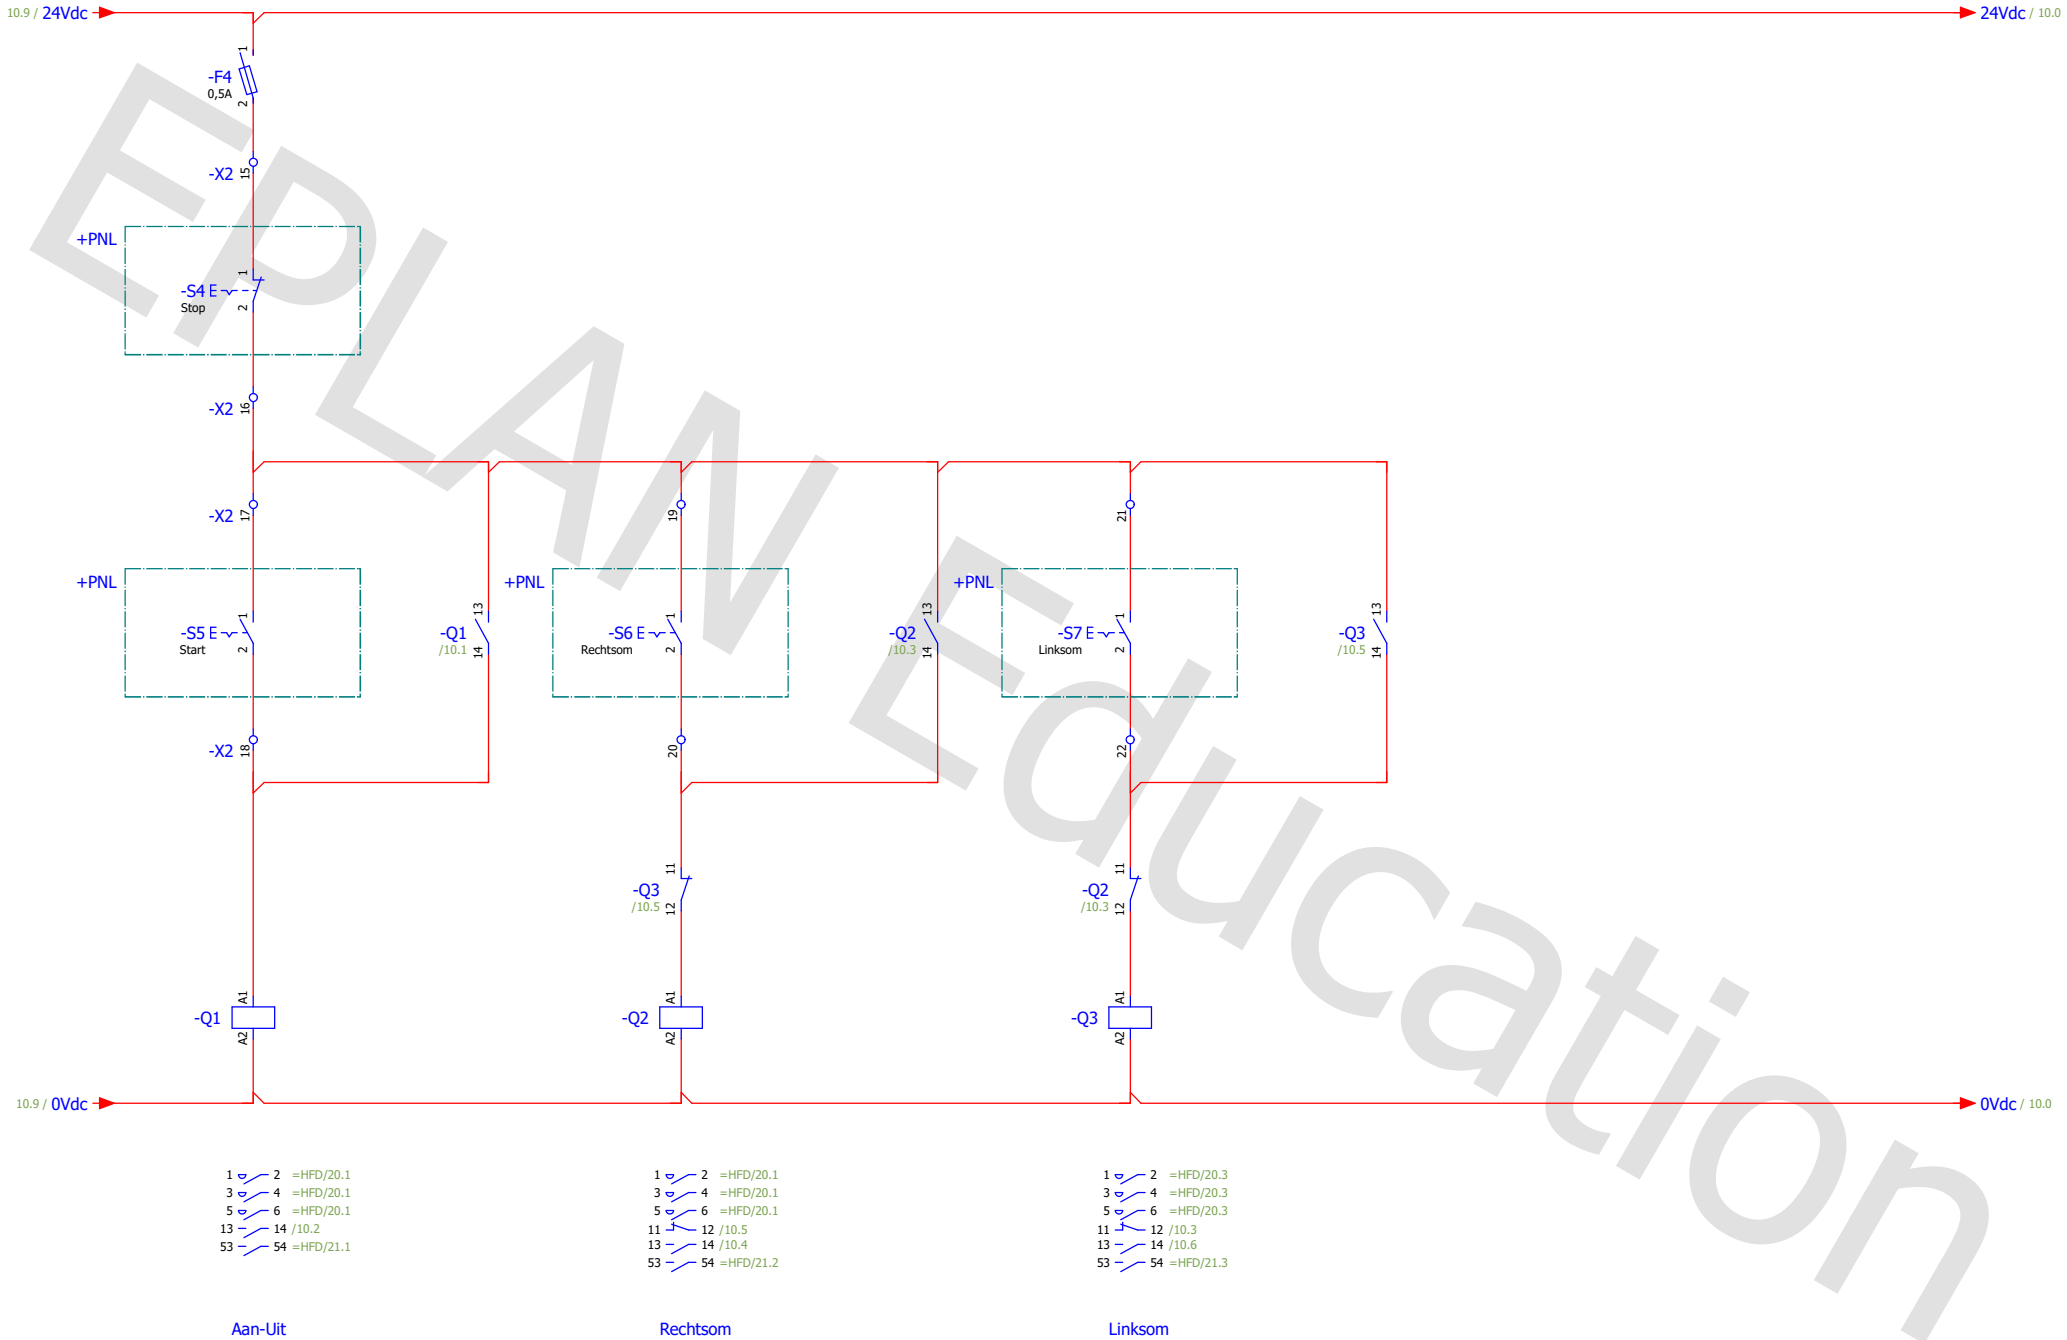

EPLAN Education

=PWR/41 =HFD/20


			Datum	16-3-2026	EPLAN	EPLAN GmbH & Co. KG	Aan-uit omkeer sturing	= STR	
			Bew.	htjid				+ ESK	
			Gecontr.		Basisproject met coderingsstructuur volgens IEC-norm: Paginastructuur met functie aanduiding en locatie aanduiding			IEC_bas001	Blad 10
Wijziging	Datum	Naam	Oorspr.		Vervanging van	Vervangen door			Pagina 4 / 6

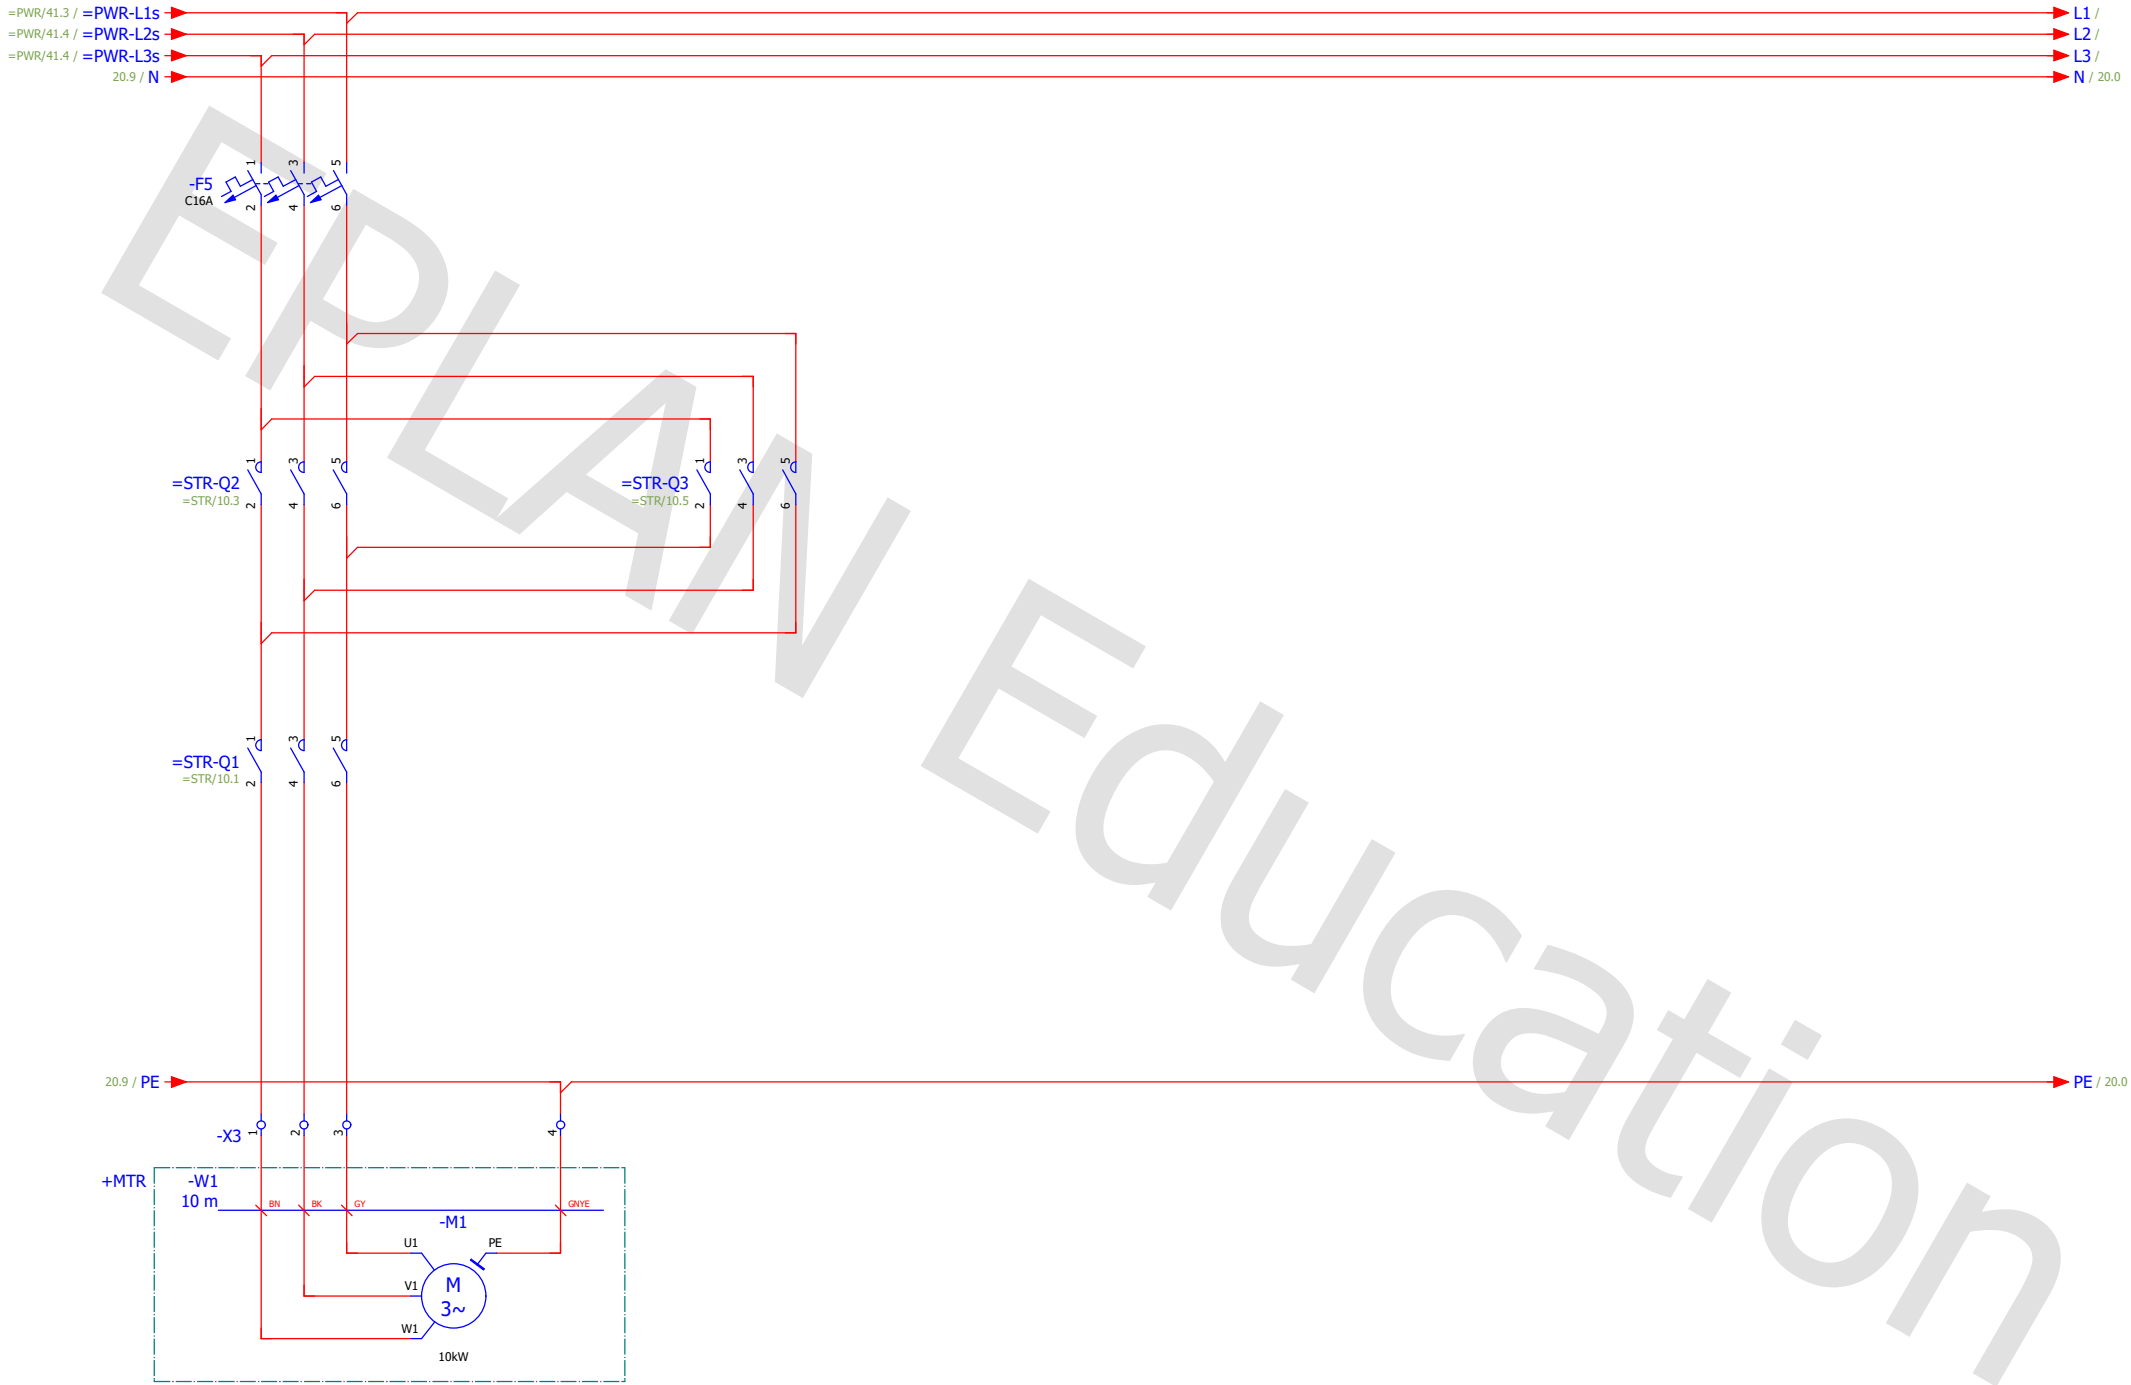

EPLAN Education

=STR/10

			Datum	25-3-2026	EPLAN	EPLAN GmbH & Co. KG	3-fase motor		= HFD
			Bew.	htjid					+ ESK
			Gecontr.		Basisproject met coderingsstructuur volgens IEC-norm: Paginastructuur met functie aanduiding en locatie aanduiding			IEC_bas001	Blad 20
Wijziging	Datum	Naam	Oorspr.		Vervanging van	Vervangen door			Pagina 5 / 6

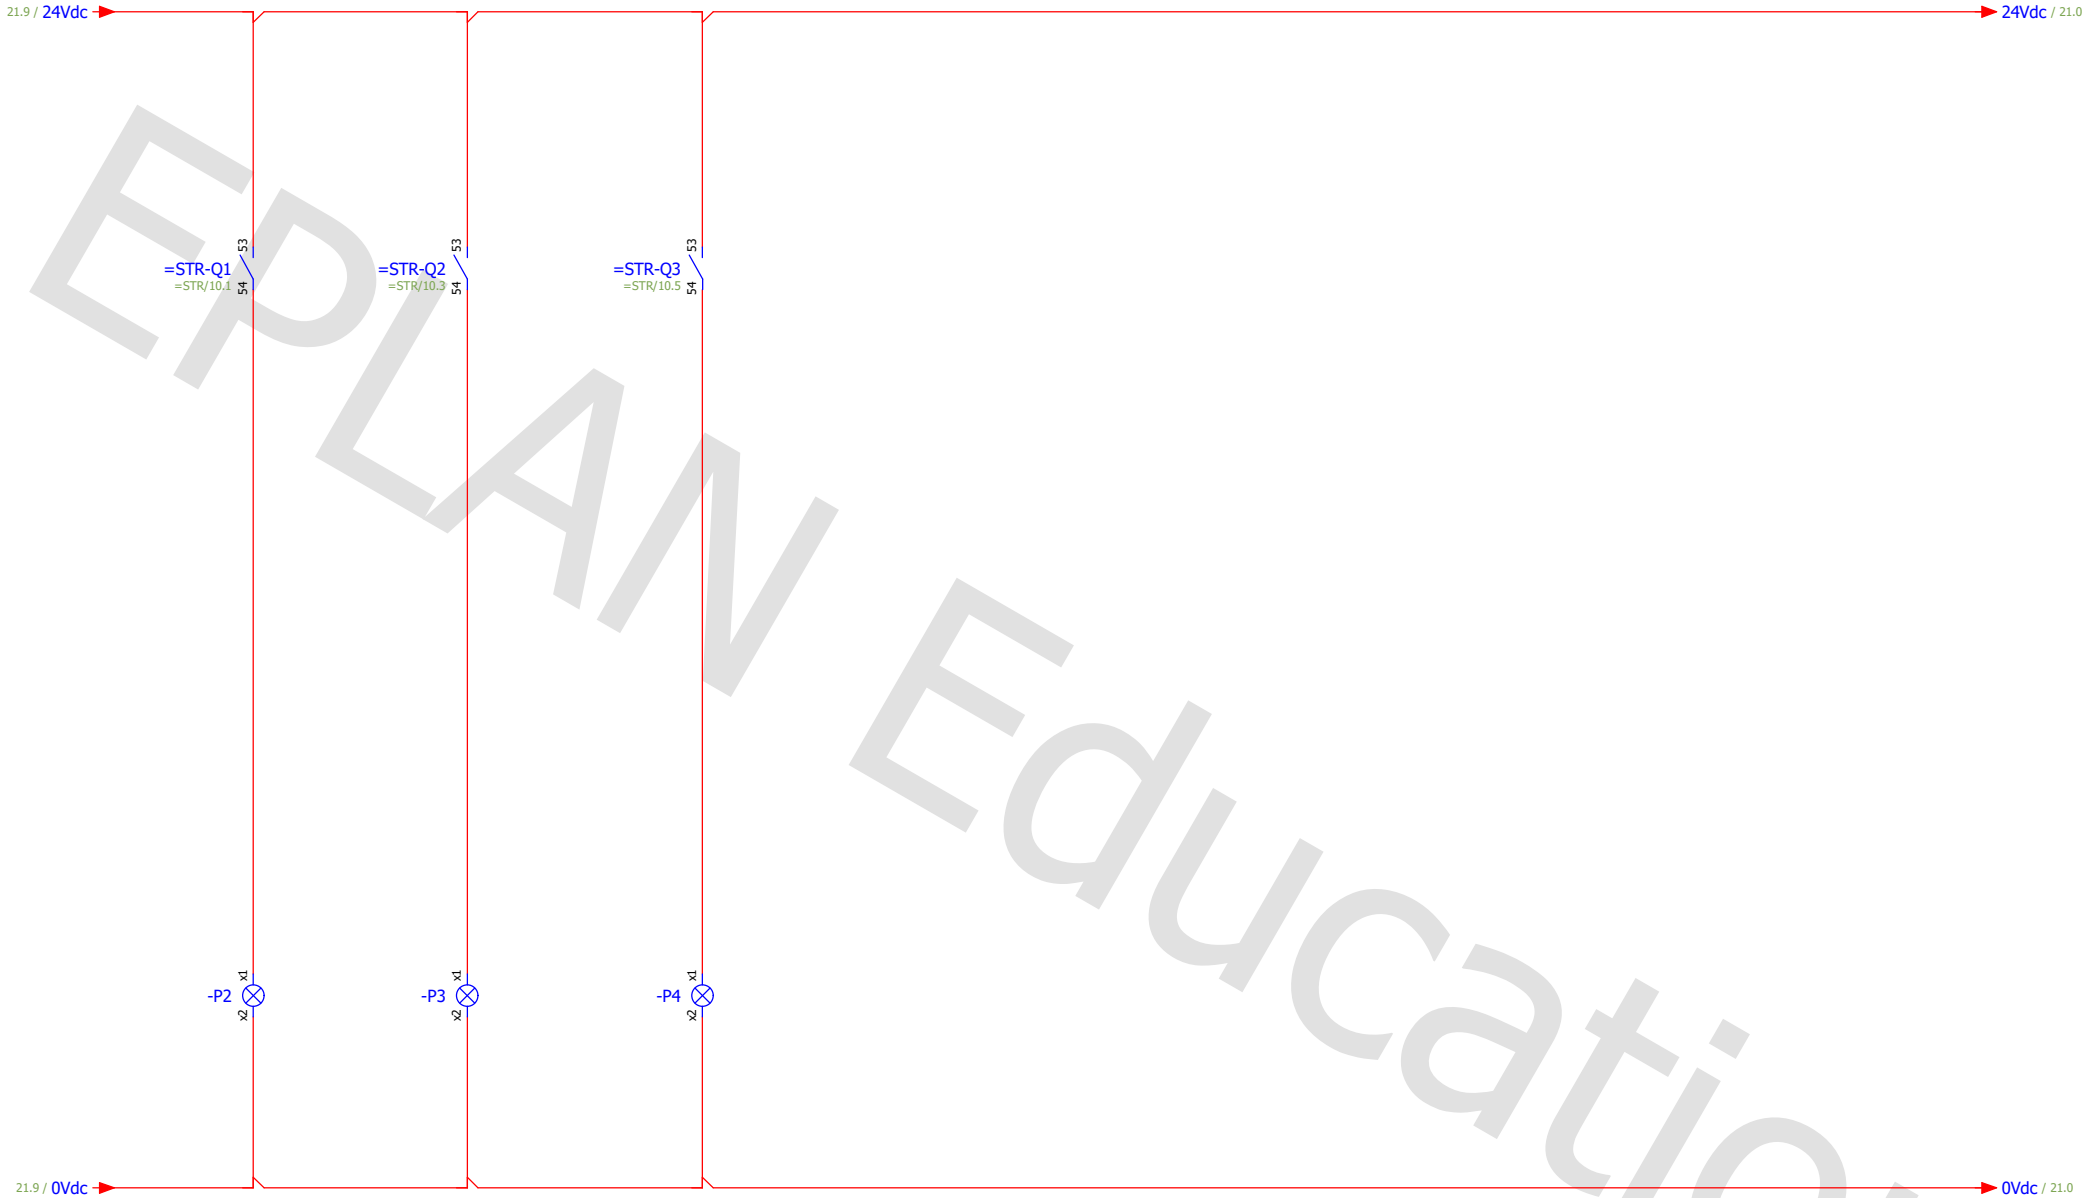

EPLAN Education

20

			Datum	16-3-2026	EPLAN	EPLAN GmbH & Co. KG	Signalering		= HFD	
			Bew.	htjid					+ ESK	
			Gecontr.		Basisproject met coderingsstructuur volgens IEC-norm: Paginastructuur met functie aanduiding en locatie aanduiding			IEC_bas001	Blad	21
Wijziging	Datum	Naam	Oorspr.		Vervanging van	Vervangen door			Pagina	6 / 6